WIDOKI ELEWACJI A-9
1:100

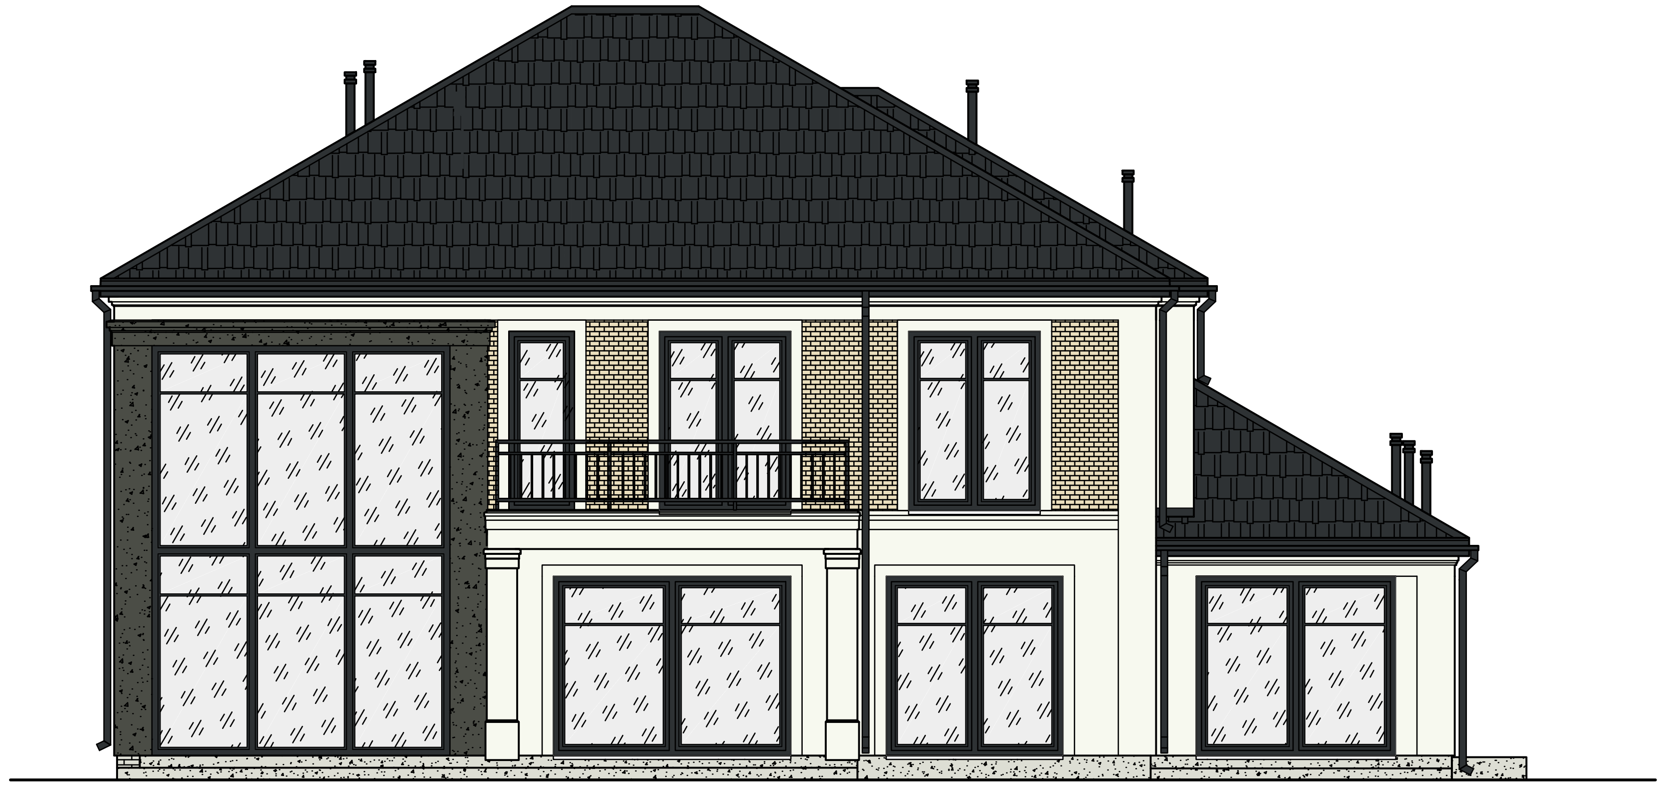

WIDOK ELEWACJI POŁUDNIOWEJ
1:100

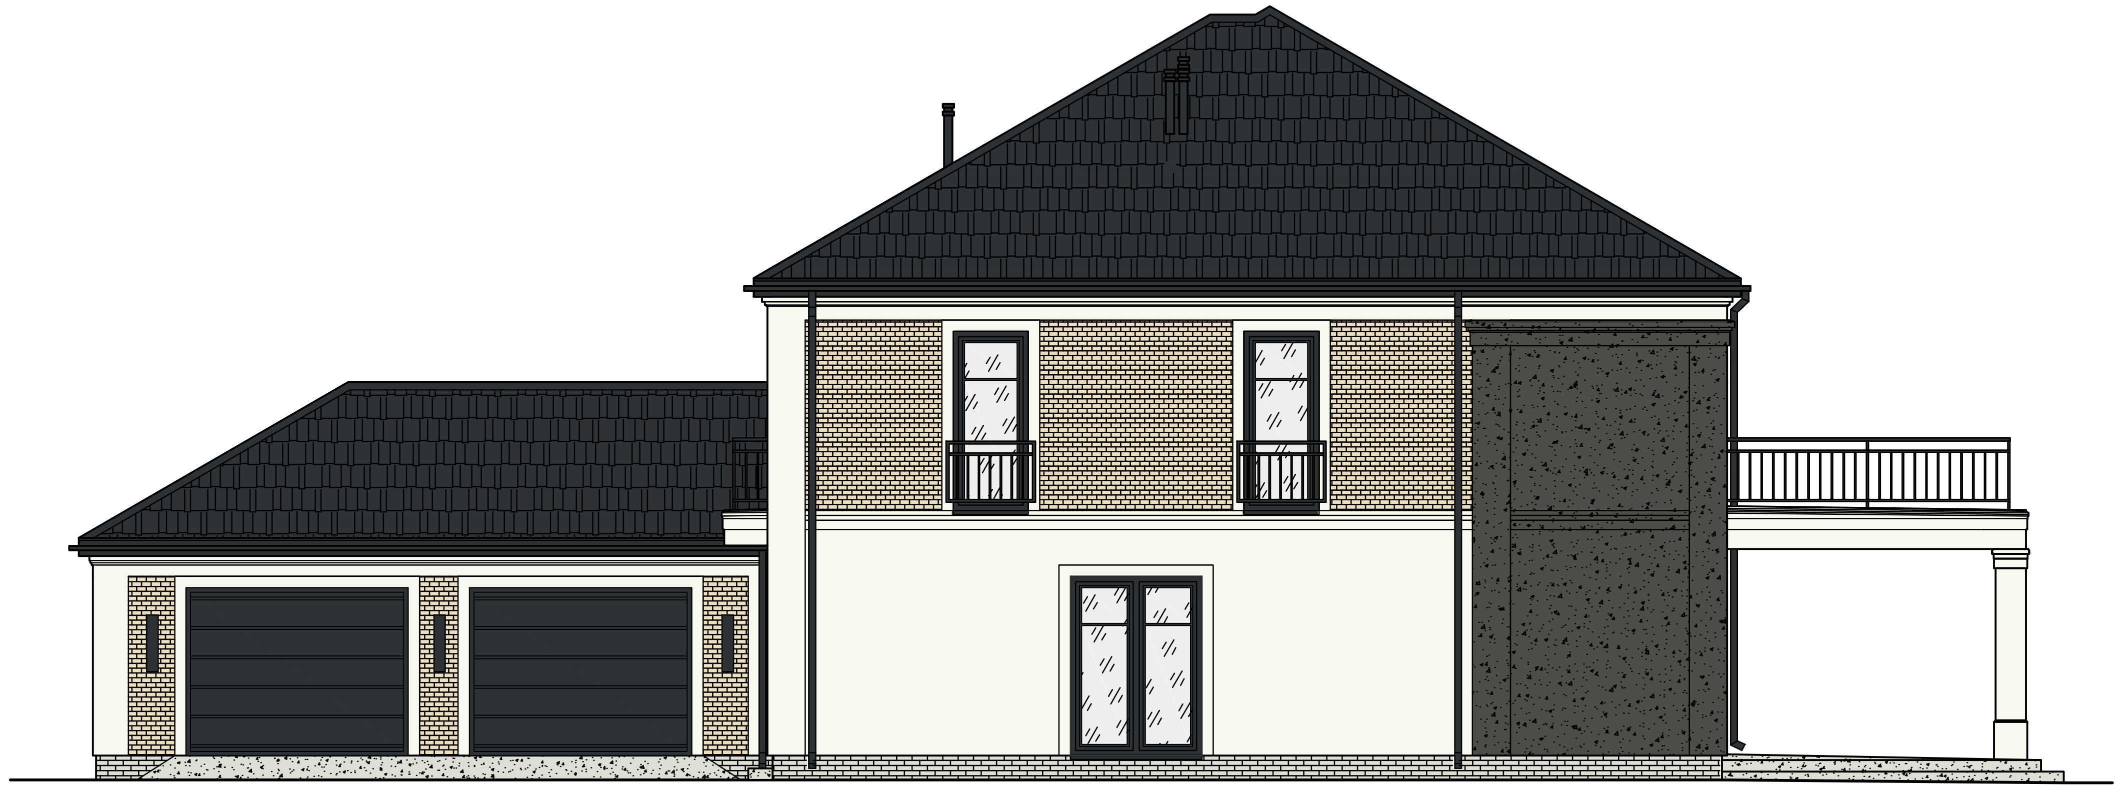

WIDOK ELEWACJI ZACHODNIEJ
1:100

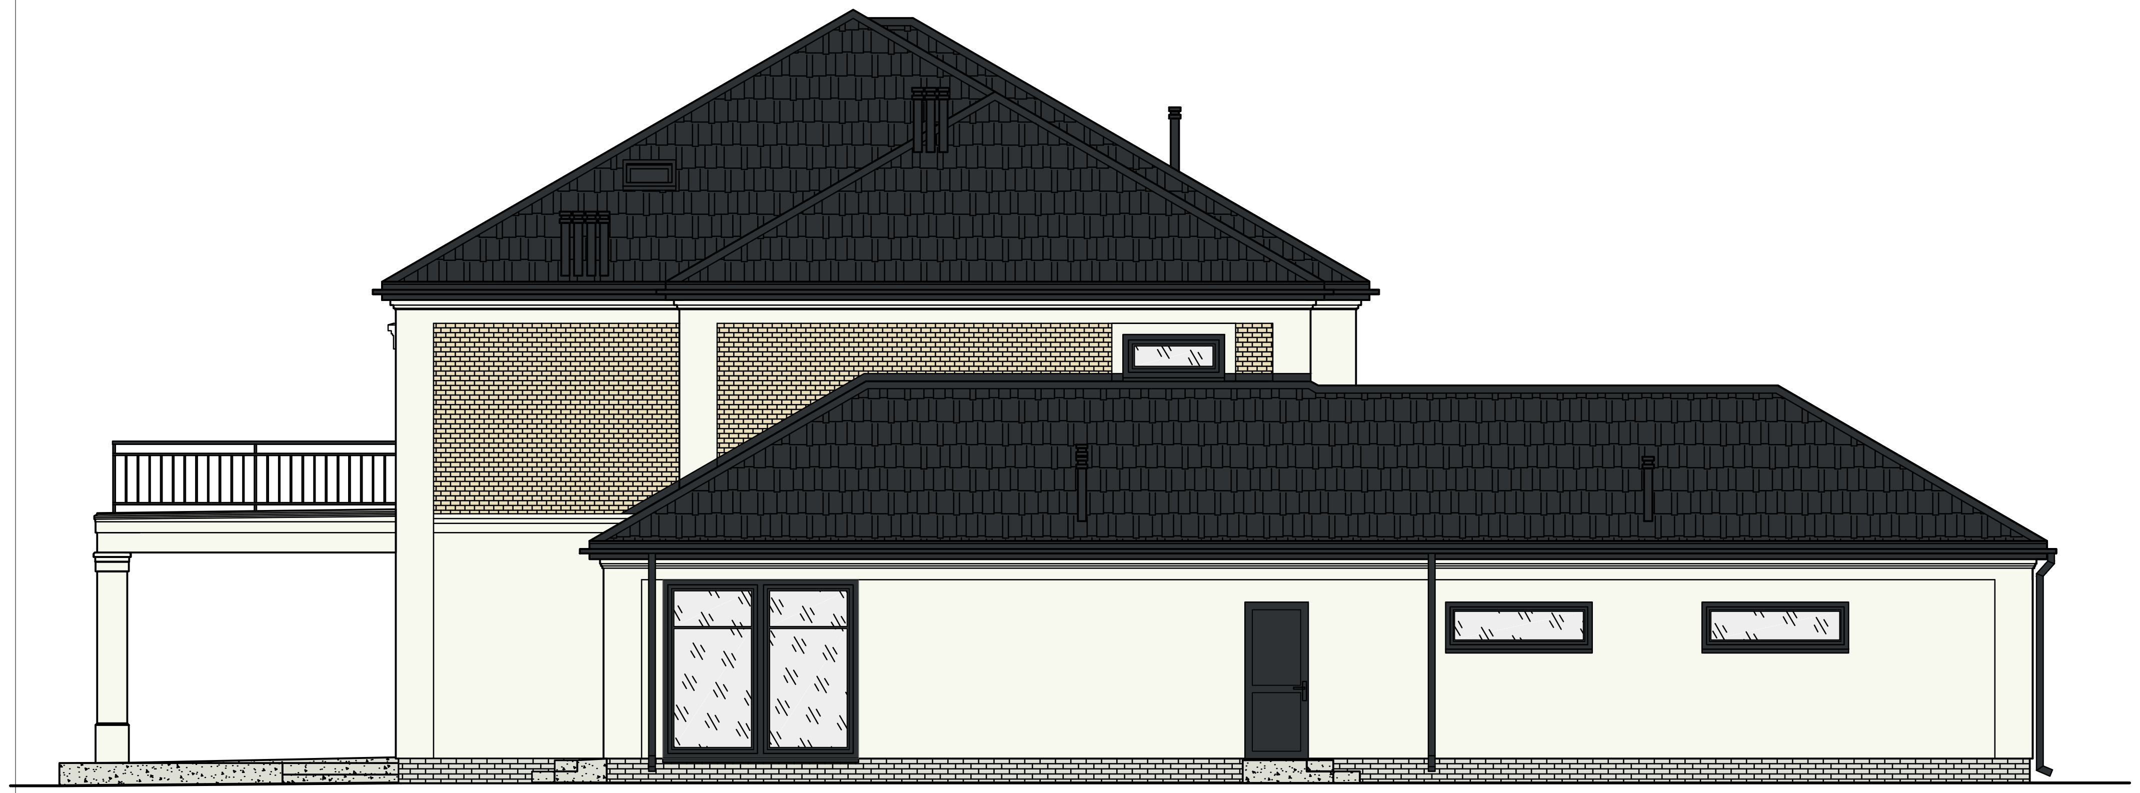

WIDOK ELEWACJI WSCHODNIEJ
1:100

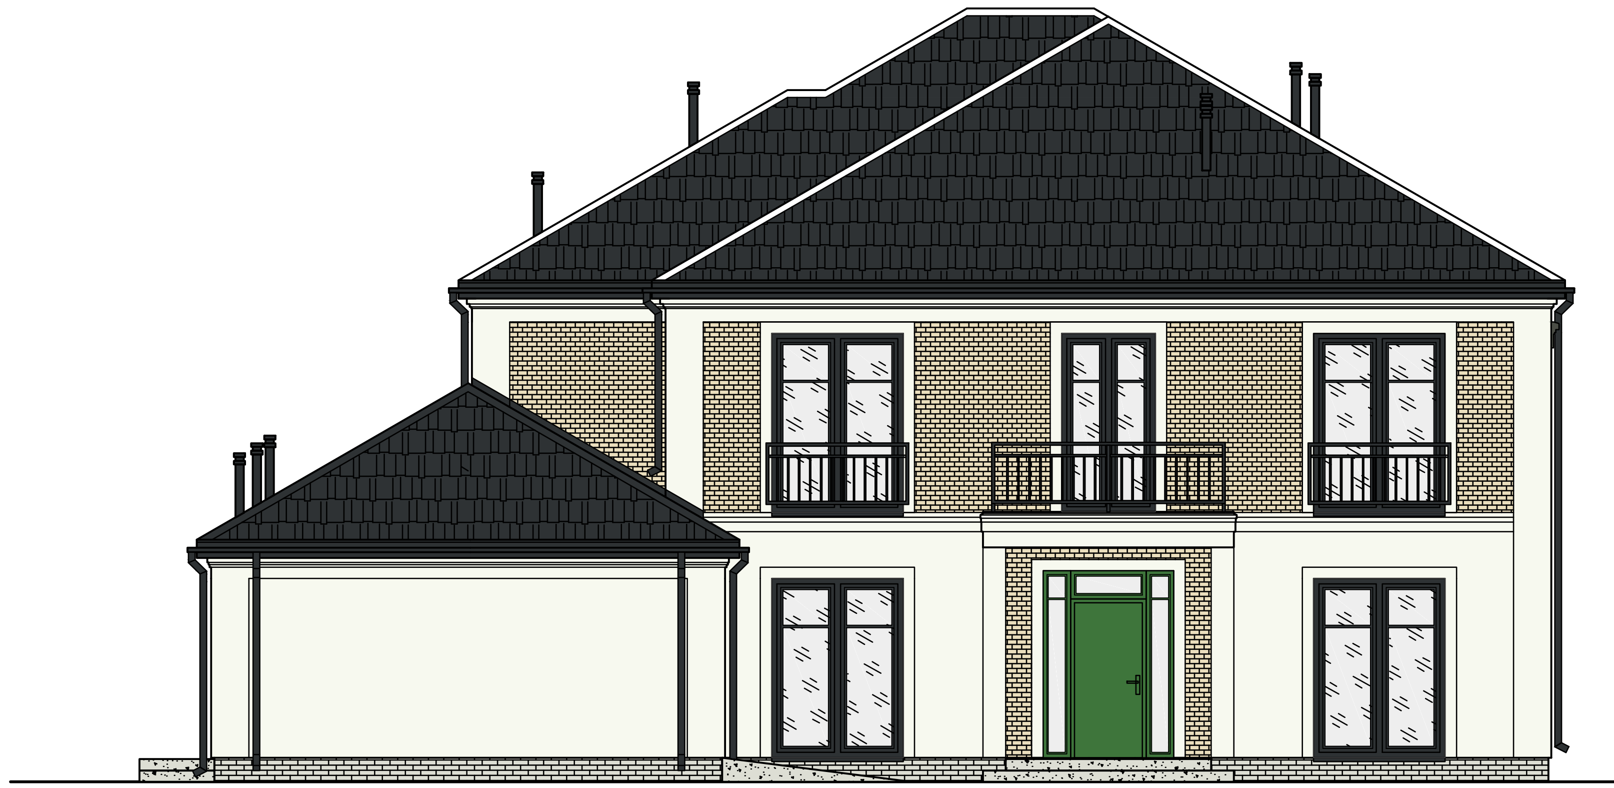

WIDOK ELEWACJI PÓŁNOCNEJ
1:100

- ☐ TYNK SILIKONOWY ZIARNO 1,5 mm, NP. CERESIT 74 W KOLORZE RAL9010
- ■ TYNK SILIKONOWY ZIARNO 1,5 mm, NP. CERESIT 74 W KOLORZE RAL7022
- ▨ KONFEKCJA BETONOWA JASNOSZARA NP. BRUKBET TRAWERTYN
- ▦ PŁYTKA KLINKIEROWA JASNOSZARA NP. KMK WARMOND 14 Z JASNĄ FUGĄ
- ▦ LICO PŁYTKI CERAMICZNEJ PIASKOWEJ NP. STEGU CAMBRIDGE 1 Z JASNĄ FUGĄ
- ▩ BLACHODACHÓWKA MODUŁOWA CIEMNOSZARA NP. RAL8022
- ■ OBRÓBKA BLACHARSKA CIEMNOSZARA NP. RAL8022
- ▧ SZKŁO
- 🟩 PVC RAL6010

BIURO PROJEKTOWE
ARTECH
Biuro Projektowe ARTECH Michał Wojno
ul. Moniuszki 19
18-300 Zambrów
tel. 692977702, e-mail artechmwojno@interia.pl
NIP: 7231629256; REGON: 200831090
www.artechmwojno.com.pl

TYTUŁ:

BUDOWA BUDYNKU MIESZKALNEGO JEDNORODZINNEGO
WRAZ Z INFRASTRUKTURĄ TOWARZYSZĄCĄ - ZBIORNIKIEM
BEZODPŁYWOWYM NA NIECZYSTOŚCI CIEKŁE O POJ. 9,9 m3

MGR INŻ. ARCH. MICHAŁ WOJNO
UPR. PROJEKT. 27/PDOKK/2016

MGR INŻ. STEFAN WOJNO
UPR. PROJEKT. UAN II 6342-70/94, UPR. KONSTR. Łom 43/86

NAZWA RYSUNKU:

WIDOKI ELEWACJI

DATA:	SKALA:	NR. RYS.
24.02.2026	1:100	A-9